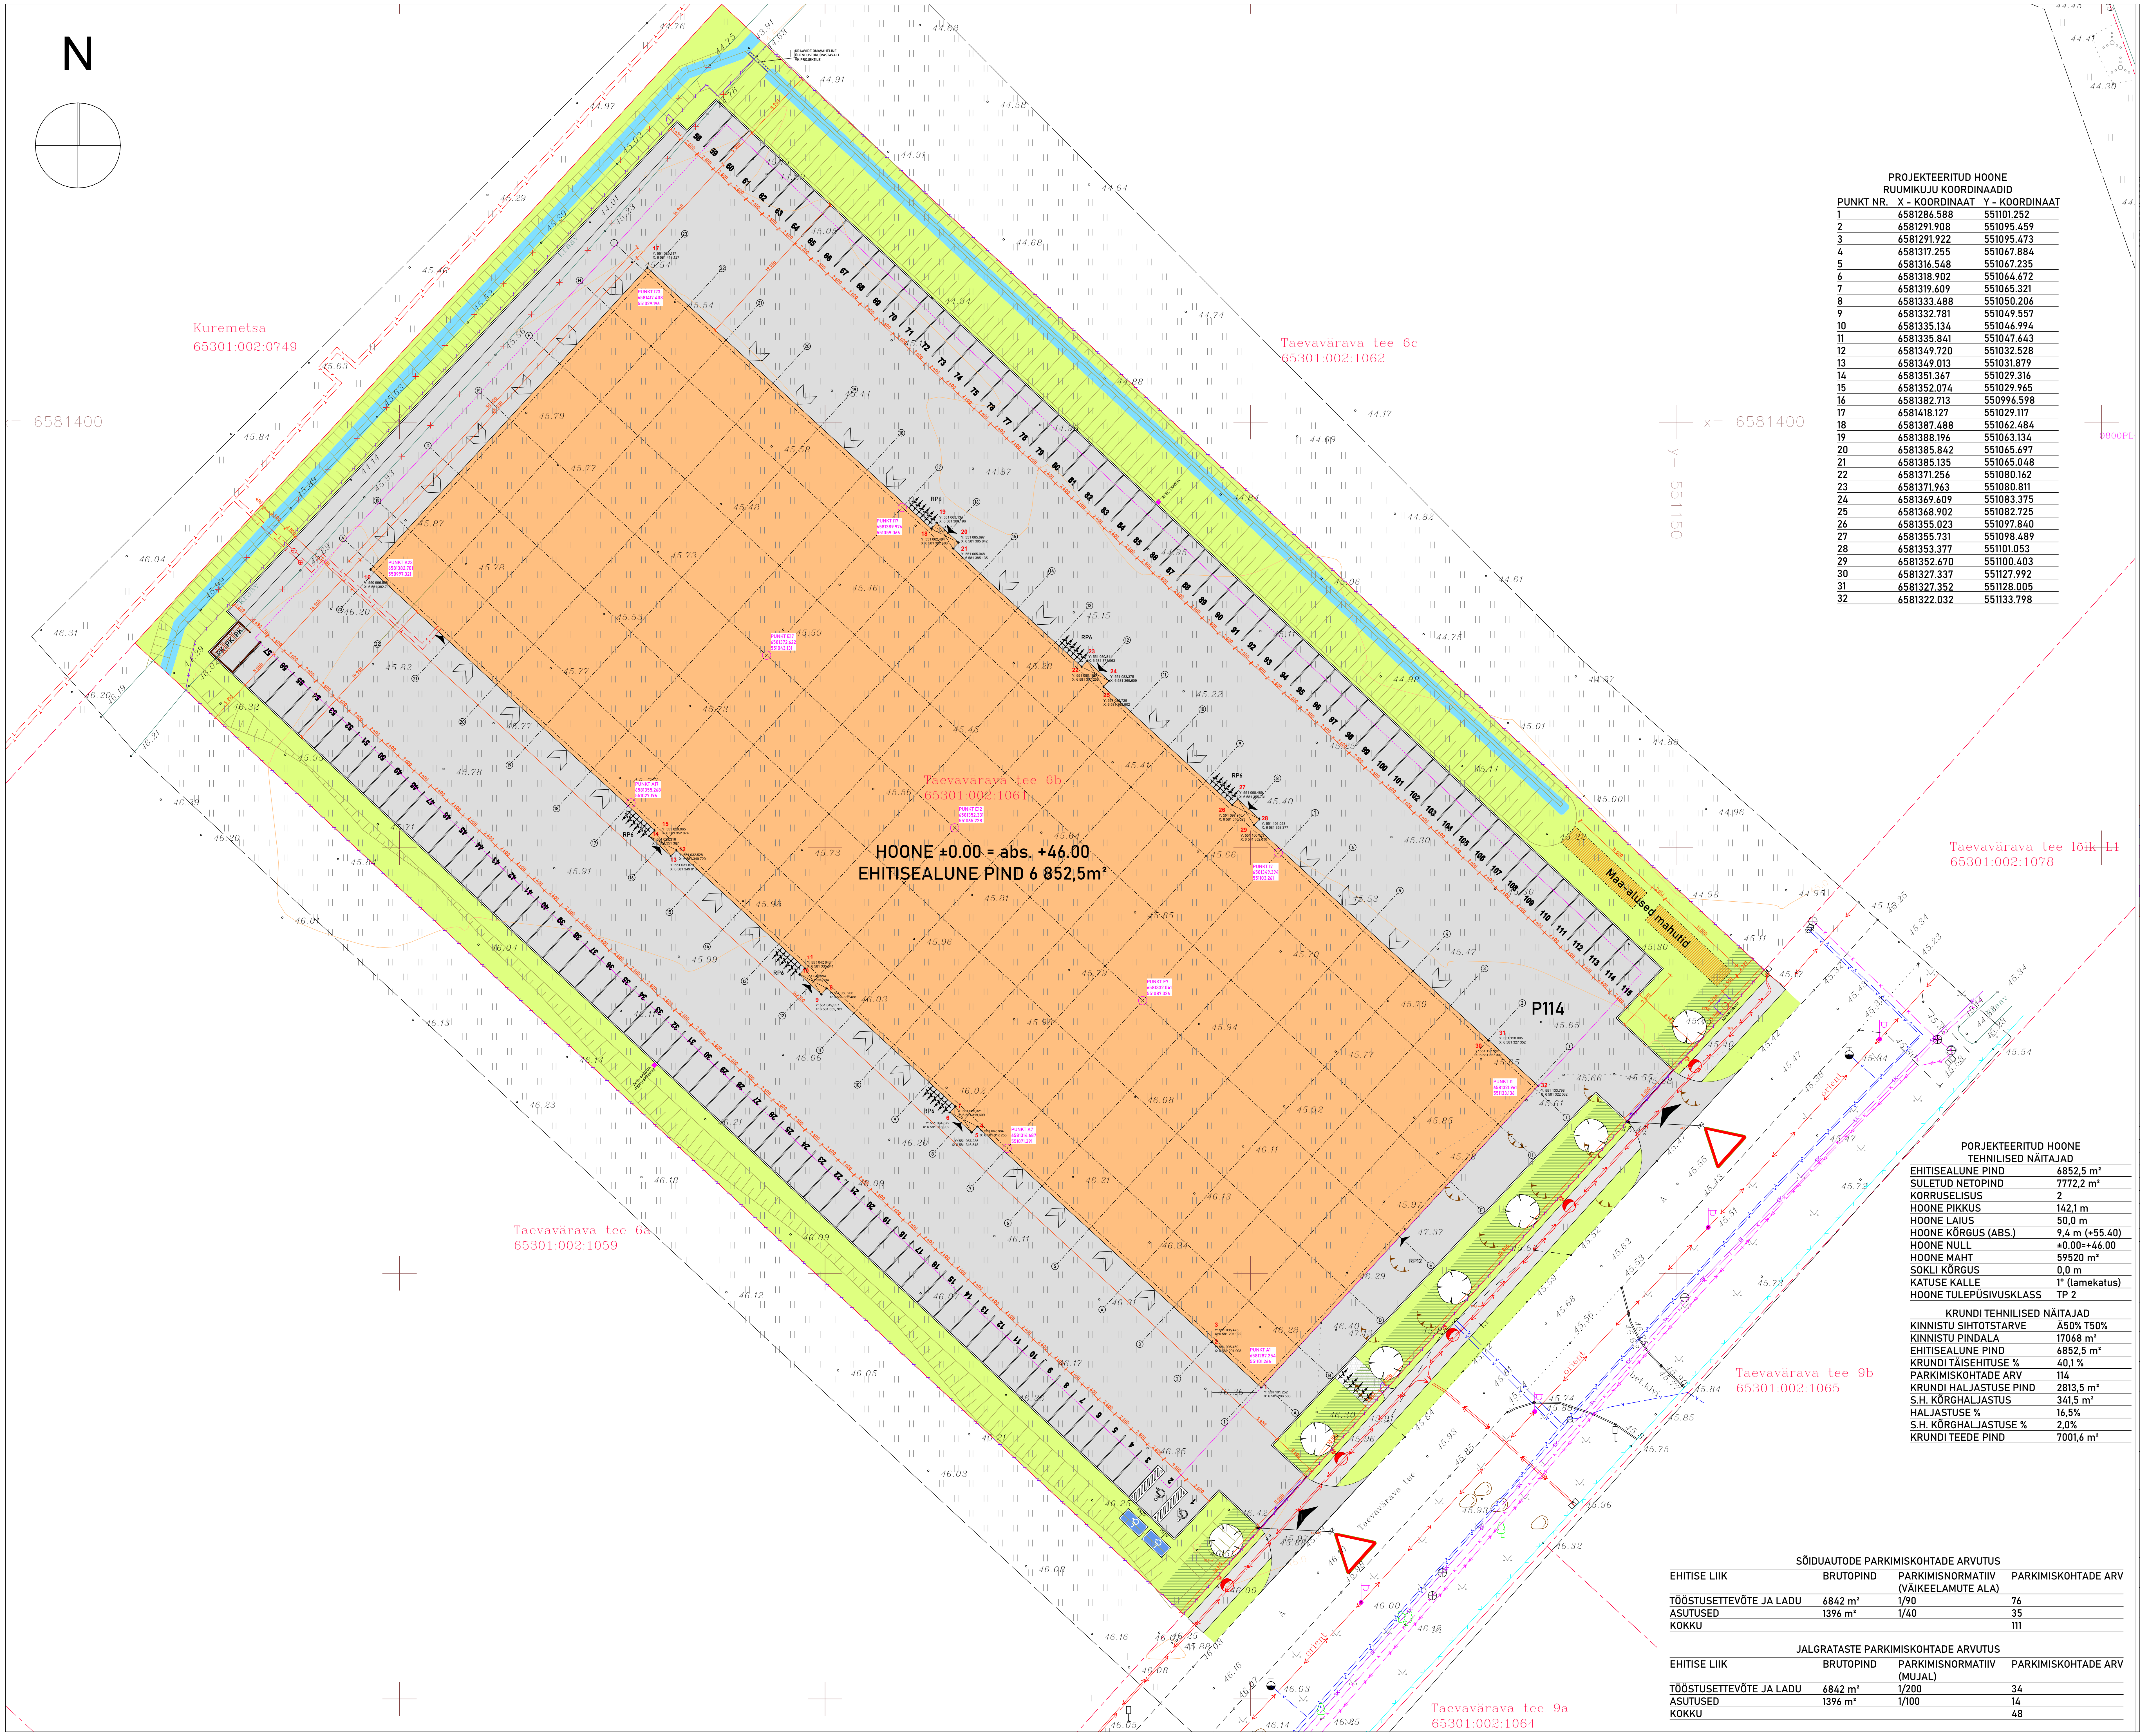

PROJEKTEERITUD HOONE
RUUMIKUJU KOORDINAADID

PUNKT NR.	X - KOORDINAAT	Y - KOORDINAAT
1	6581286.588	551101.252
2	6581291.908	551095.459
3	6581291.922	551095.473
4	6581317.255	551067.884
5	6581316.548	551067.235
6	6581318.902	551064.672
7	6581319.609	551065.321
8	6581333.488	551050.206
9	6581332.781	551049.557
10	6581335.134	551046.994
11	6581335.841	551047.643
12	6581349.720	551032.528
13	6581349.013	551031.879
14	6581351.367	551029.316
15	6581352.074	551029.965
16	6581382.713	550996.598
17	6581418.127	551029.117
18	6581387.488	551062.484
19	6581388.196	551063.134
20	6581385.842	551065.697
21	6581385.135	551065.048
22	6581371.256	551080.162
23	6581371.963	551080.811
24	6581369.609	551083.375
25	6581368.902	551082.725
26	6581355.023	551097.840
27	6581355.731	551098.489
28	6581353.377	551101.053
29	6581352.670	551100.403
30	6581327.337	551127.992
31	6581327.352	551128.005
32	6581322.032	551133.798

MÄRKUSED:
KÄESOLEVAT JOONIST TULEB KÄSITLEDA KOOS KÕIKIDE TEISTE EHITUSPROJEKTI OSADEGA. PROJEKTEERITUD OSADE JA NENDE OMAVAHELISTE VASTUOLUDE, EBATÄPSUSTE JA KÜSIMUSTE ILMNEMISEL TULEB KOHE VÕTTA ÜHENDUST PROJEKTEERIJAGA. KÕIKIDE MATERJALIDE JA EHITUSTÖÖDE KVALITEET PEAB VASTAMA EESTI VABARIIGIS KEHTIVATELE SEADUSANDLIKE AKTIDE JÄRGI KEHTESTATUD NÕUETELE JA OLEMA KOOSKÕLAS HEA EHITUSTAVAGA. TOOTEID TULEB KÄSITLEDA JA KASUTADA VASTAVALT TOOTJAPOOLSETELE NÕUETELE, SOOVITUSTELE, HEALE EHITUSTAVALE JA EHITUSNORMIDELE. KÕIK EHITUSAEGSED MISTAHES EHITUSPROJEKTI OSAS NÄIDATUD LAHENDUSTE MUUDATUSED TULEB KÕIGEPEALT KOOSKÕLASTADA PROJEKTEERIJAGA NING SEEJÄREL TELLIJAGA.

ANTUD JOONIS ON KAITSTUD AUTORIÕIGUSEGA. SELLE KOPEERIMINE, LEVITAMINE, REPRODUTSEERIMINE, SAMUTI SELLES MUUDATUSTE TEGEMINE ILMA AUTORIÕIGUSTE VALDAJA LOATA ON KEELATUD. JOONIS VÕIB SISALDADA KONFIDENTSIAALSET INFORMATSIOONI, MILLE TAHTLIK LEVITAMINE ON KARISTATAV. ENNE TEOSTAMIST KONTROLLIDA UUEMA VÄLJAANDE OLEMASOLU! HILISEMA KUUPÄEVAGA JOONIS TÜHISTAB VARASEMA. KÕIK MÕÕDUD JA KÕRGUSMÄRGID KONTROLLIDA EHITUSEL.

TAEVAVÄRAVA TEE 6B KINNISTU TINGMÄRGID:

	KINNISTUPIIR
	DP EHITUSALA PIIR
kraav	OLEMASOLEV KRAAV
kraav	NIHUTATAV KRAAVI LÕIK
🟧	PROJ. HOONE
▨	PROJ. HOONE VARIKATUSE OSA
⬛	PROJ. SÕIDUTEE / ASFALTBETOONKATE
⬜	PROJ. KÕNNITEE / ASFALTBETOONKATE
▦	PROJ. KÕNNITEE / BETOONIKIVI KATEND
🟩	PROJ. HALJASALA
🟦	PROJ. KRAAV
▨	PROJ. HALJASALA + KÕRGHALJASTUS
▨	PROJ. MAA-ALUNE MAHUTI
PK PK PK	PROJ. PRÜGIKONTEINERID JA PIIRE h=1,5m
1 2 3 4	PROJ. HOONE NURGAPUNKTID
P115	PROJ. PARKIMISKOHAD JA ARV
RP12	PROJ. JALGRATTA PARKIMISKOHAD JA ARV
▲	SISSEPÄÄSUD KINNISTULE / HOONESSE
○ ○ ○ ○	PROJ. KÕRGHALJASTUS (POOPPUU)
	PROJ. KEEVISPANEEL AIAPIIRE h=1,8 M
	PROJ. JALGVÄRAV
	PROJ. LIUGVÄRAV
🟪	2x EL.LAADIJA ASUKOHT
«	LADUDE SISSESÕIT
575d	LIIKLUSMÄRK - PUUDEGA INIMESE SÕIDUKI PARKIMISKOHT (575d)
221	LIIKLUSMÄRK - ANNA TEED (221)
●	PROJ. VALGUSTI, NT VFL520 KÕRGUS 8M
	OLEMASOLEV MADALPINGEKAABEL
V	OLEMASOLEV VEETORUSTIK
K	OLEMASOLEV REOVEE TORUSTIK
	OLEMASOLEV REOVEE SURVETORUSTIK
SK	OLEMASOLEV SADEMEVEE TORUSTIK
T ⊕	HG PROSOLUTION OÜ PROJEKTREERITUD KAUGKÜTTETORUSTIK + KAEVUD, TÖÖ NR. HGP22007

PORJEKTEERITUD HOONE
TEHNILISED NÄITAJAD

EHITISEALUNE PIND	6852,5 m²
SULETUD NETOPIND	7772,2 m²
KORRUSELISUS	2
HOONE PIKKUS	142,1 m
HOONE LAIUS	50,0 m
HOONE KÕRGUS (ABS.)	9,4 m (+55.40)
HOONE NULL	±0.00=+46.00
HOONE MAHT	59520 m³
SOKLI KÕRGUS	0,0 m
KATUSE KALLE	1° (lamekatus)
HOONE TULEPÜSIVUSKLASS	TP 2

KRUNDI TEHNILISED NÄITAJAD

KINNISTU SIHTOTSTARVE	Ä50% T50%
KINNISTU PINDALA	17068 m²
EHITISEALUNE PIND	6852,5 m²
KRUNDI TÄISEHITUSE %	40,1 %
PARKIMISKOHTADE ARV	114
KRUNDI HALJASTUSE PIND	2813,5 m²
S.H. KÕRGHALJASTUS	341,5 m²
HALJASTUSE %	16,5%
S.H. KÕRGHALJASTUSE %	2,0%
KRUNDI TEEDE PIND	7001,6 m²

SÕIDUAUTODE PARKIMISKOHTADE ARVUTUS

EHITISE LIIK	BRUTOPIND	PARKIMISNORMATIIV (VÄIKEELAMUTE ALA)	PARKIMISKOHTADE ARV
TÖÖSTUSETTEVÕTE JA LADU	6842 m²	1/90	76
ASUTUSED	1396 m²	1/40	35
KOKKU			111

JALGRATASTE PARKIMISKOHTADE ARVUTUS

EHITISE LIIK	BRUTOPIND	PARKIMISNORMATIIV (MUJAL)	PARKIMISKOHTADE ARV
TÖÖSTUSETTEVÕTE JA LADU	6842 m²	1/200	34
ASUTUSED	1396 m²	1/100	14
KOKKU			48

R#	M#	Muudatus	Kuupäev

Projekti nimi:
T6B multifunktsionaalne büroo- ja laohoone

Projekti aadress:
Taevavärava tee 6b Lehmja küla Rae vald Harju maakond Eesti

Tellija:
Taevavärava OÜ
janar@futureinvest.info
+372 51926218

Töö number:
21011

Joonise nimi:
ASENDIPLAAN

Joonise number:
AS-4-02

Mõõtkava:	Staadium:	Print:	Kuupäev:
1:500	PP	A2	21.03.2023

Projekteeris(id):
Daria Olovyannikova, Karl Kiisel

Vastutav spetsialist:
Karl Kiisel
karl@dokk.ee
+372 5511658

Projektijuht:
Karl Kiisel
karl@dokk.ee
+372 5511658

Arhitekt:
DOKK
ARCHITECTS

DOKK Architects OÜ | reg nr. 14436116 | info@dokkarchitects.com
Oja 19, 13516 Tallinn, Estonia